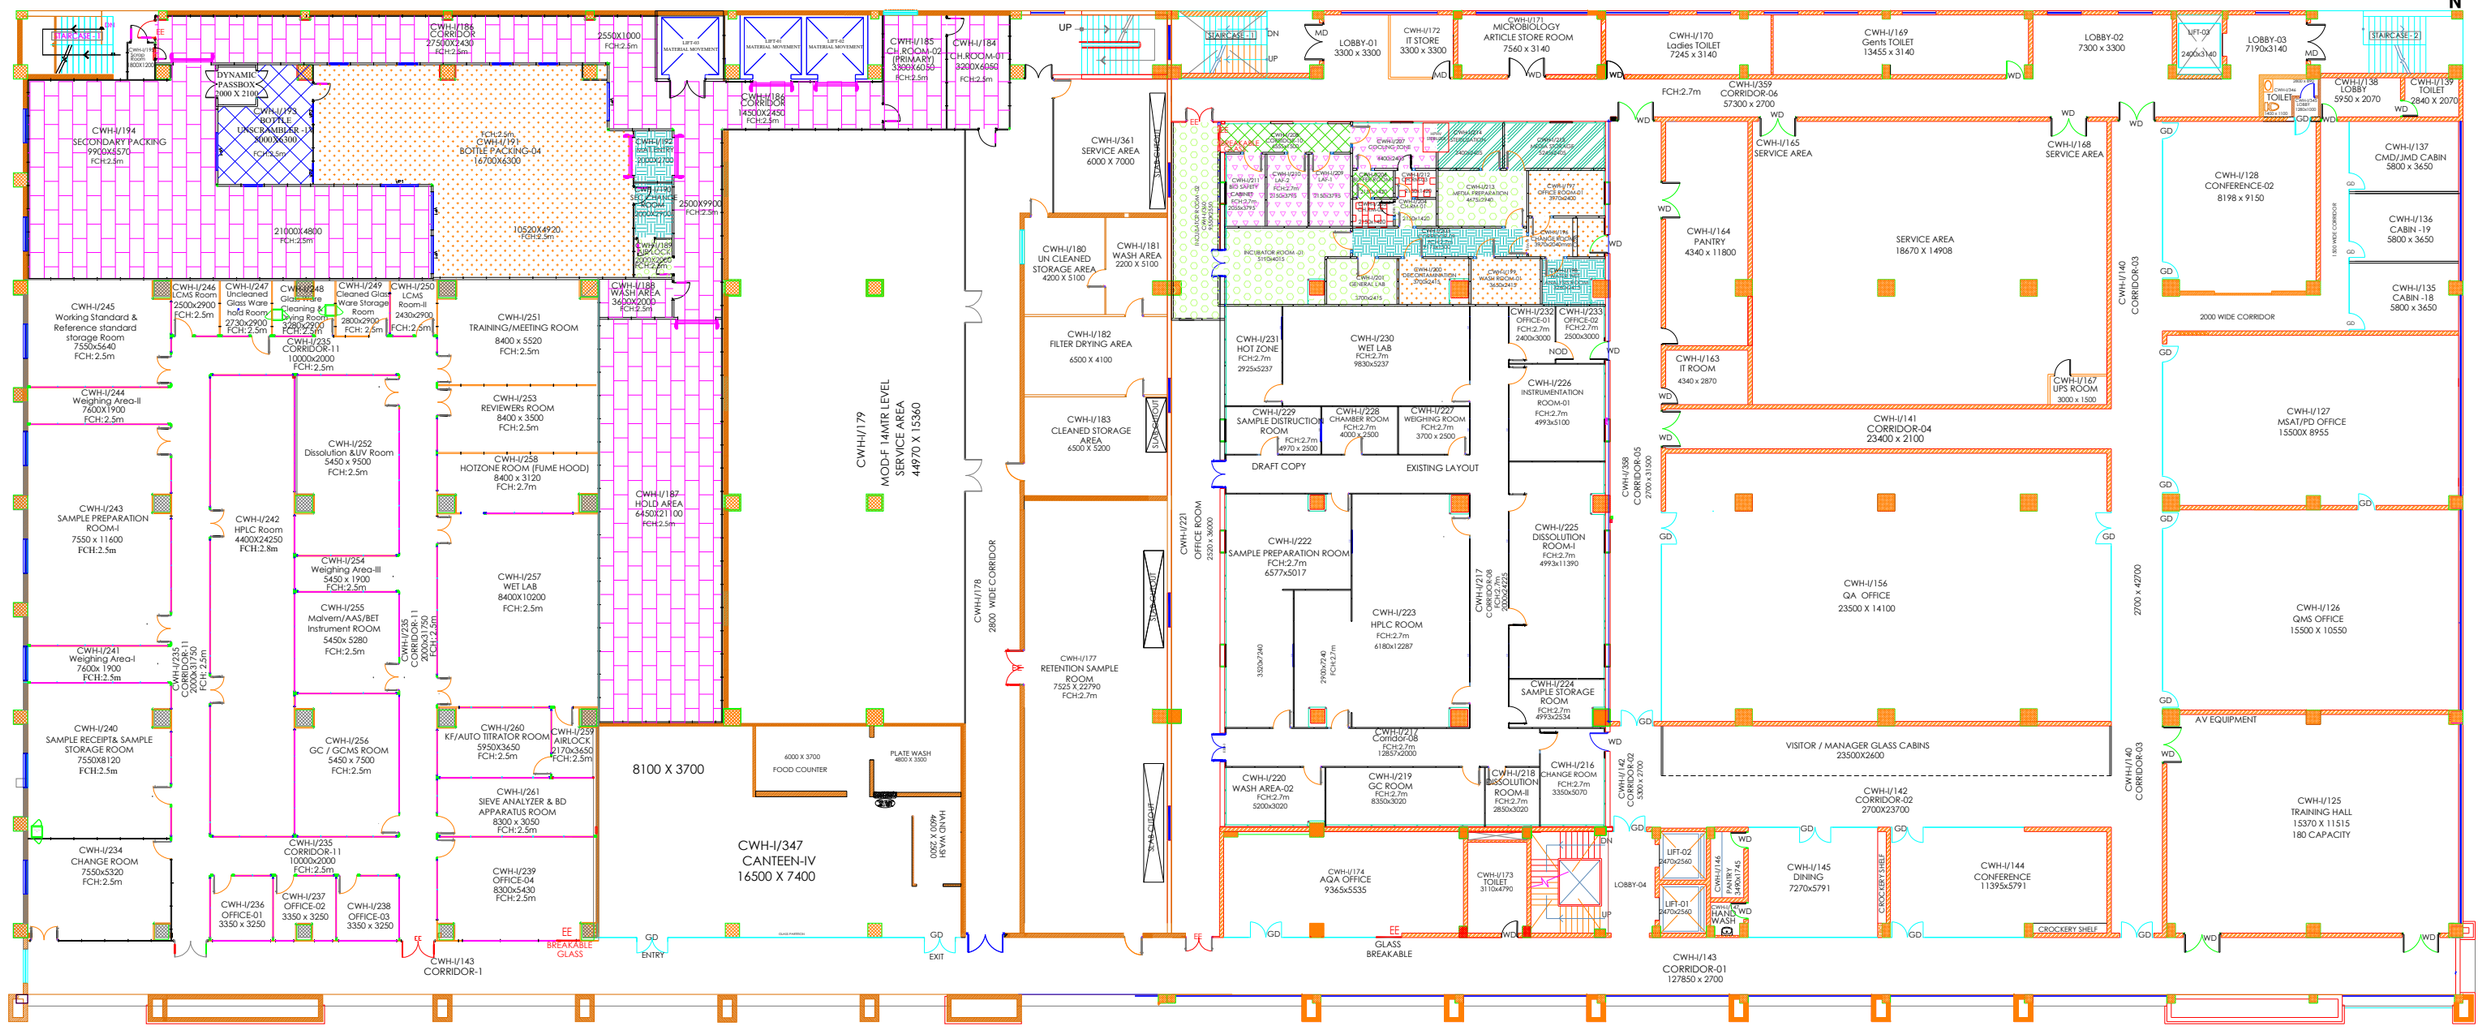


LEGEND

+VE	−VE
NLT 0.6 MM OF WC WRT	
NLT 1.5 MM OF WC WRT	
NLT 1.5 MM OF WC WRT	
NLT 0.6 MM OF WC WRT	
NLT 1.5 MM OF WC WRT	
NLT 0.6 MM OF WC WRT	

+VE	−VE
NLT 1.5 MM OF WC WRT CORRIDOR−05	
NLT 0.6 MM OF WC WRT	
NLT 0.6 MM OF WC WRT	
NLT 0.6 MM OF WC WRT	
NLT 1.0 MM OF WC WRT	

−5pa	−35pa
−15pa	−45pa
−20pa	−50pa
−25pa	−55pa
−30pa	−55pa

Granules India Limited
Sy No.160/A,161/E,162 &174/A,Gagillapur Village,Dundigal-Gandimaisamma Mandal, Medchal-Malkajgiri District - 500 043, Telangana, India

	DEPT	SIGN	DATE
DRAWN	ENGINEERING		
CHECKED	ENGINEERING		
REVIEWED	HR & ADMIN		
APPROVED	QUALITY ASSURANCE		

DRG.TITLE
CWH BLOCK
THIRD FLOOR
DIFFERENTIAL PRESSURE
ZONING LAYOUT

DRG.NO: GGP/CWH/022

REV 01